

福祉の至急条例1.257
導線確保 (1200mm幅)
※1200mm幅を確保すれば
区画内どこも通じモOK.

閉店後に什器も店内へ
移動するた客席として使用可能.


閉店後この導線は
什器設置不可.

■凡例

リースライン

消防避難導線
(1500mm幅)

腰壁は避難導線に
合わせてA工事に撤去.

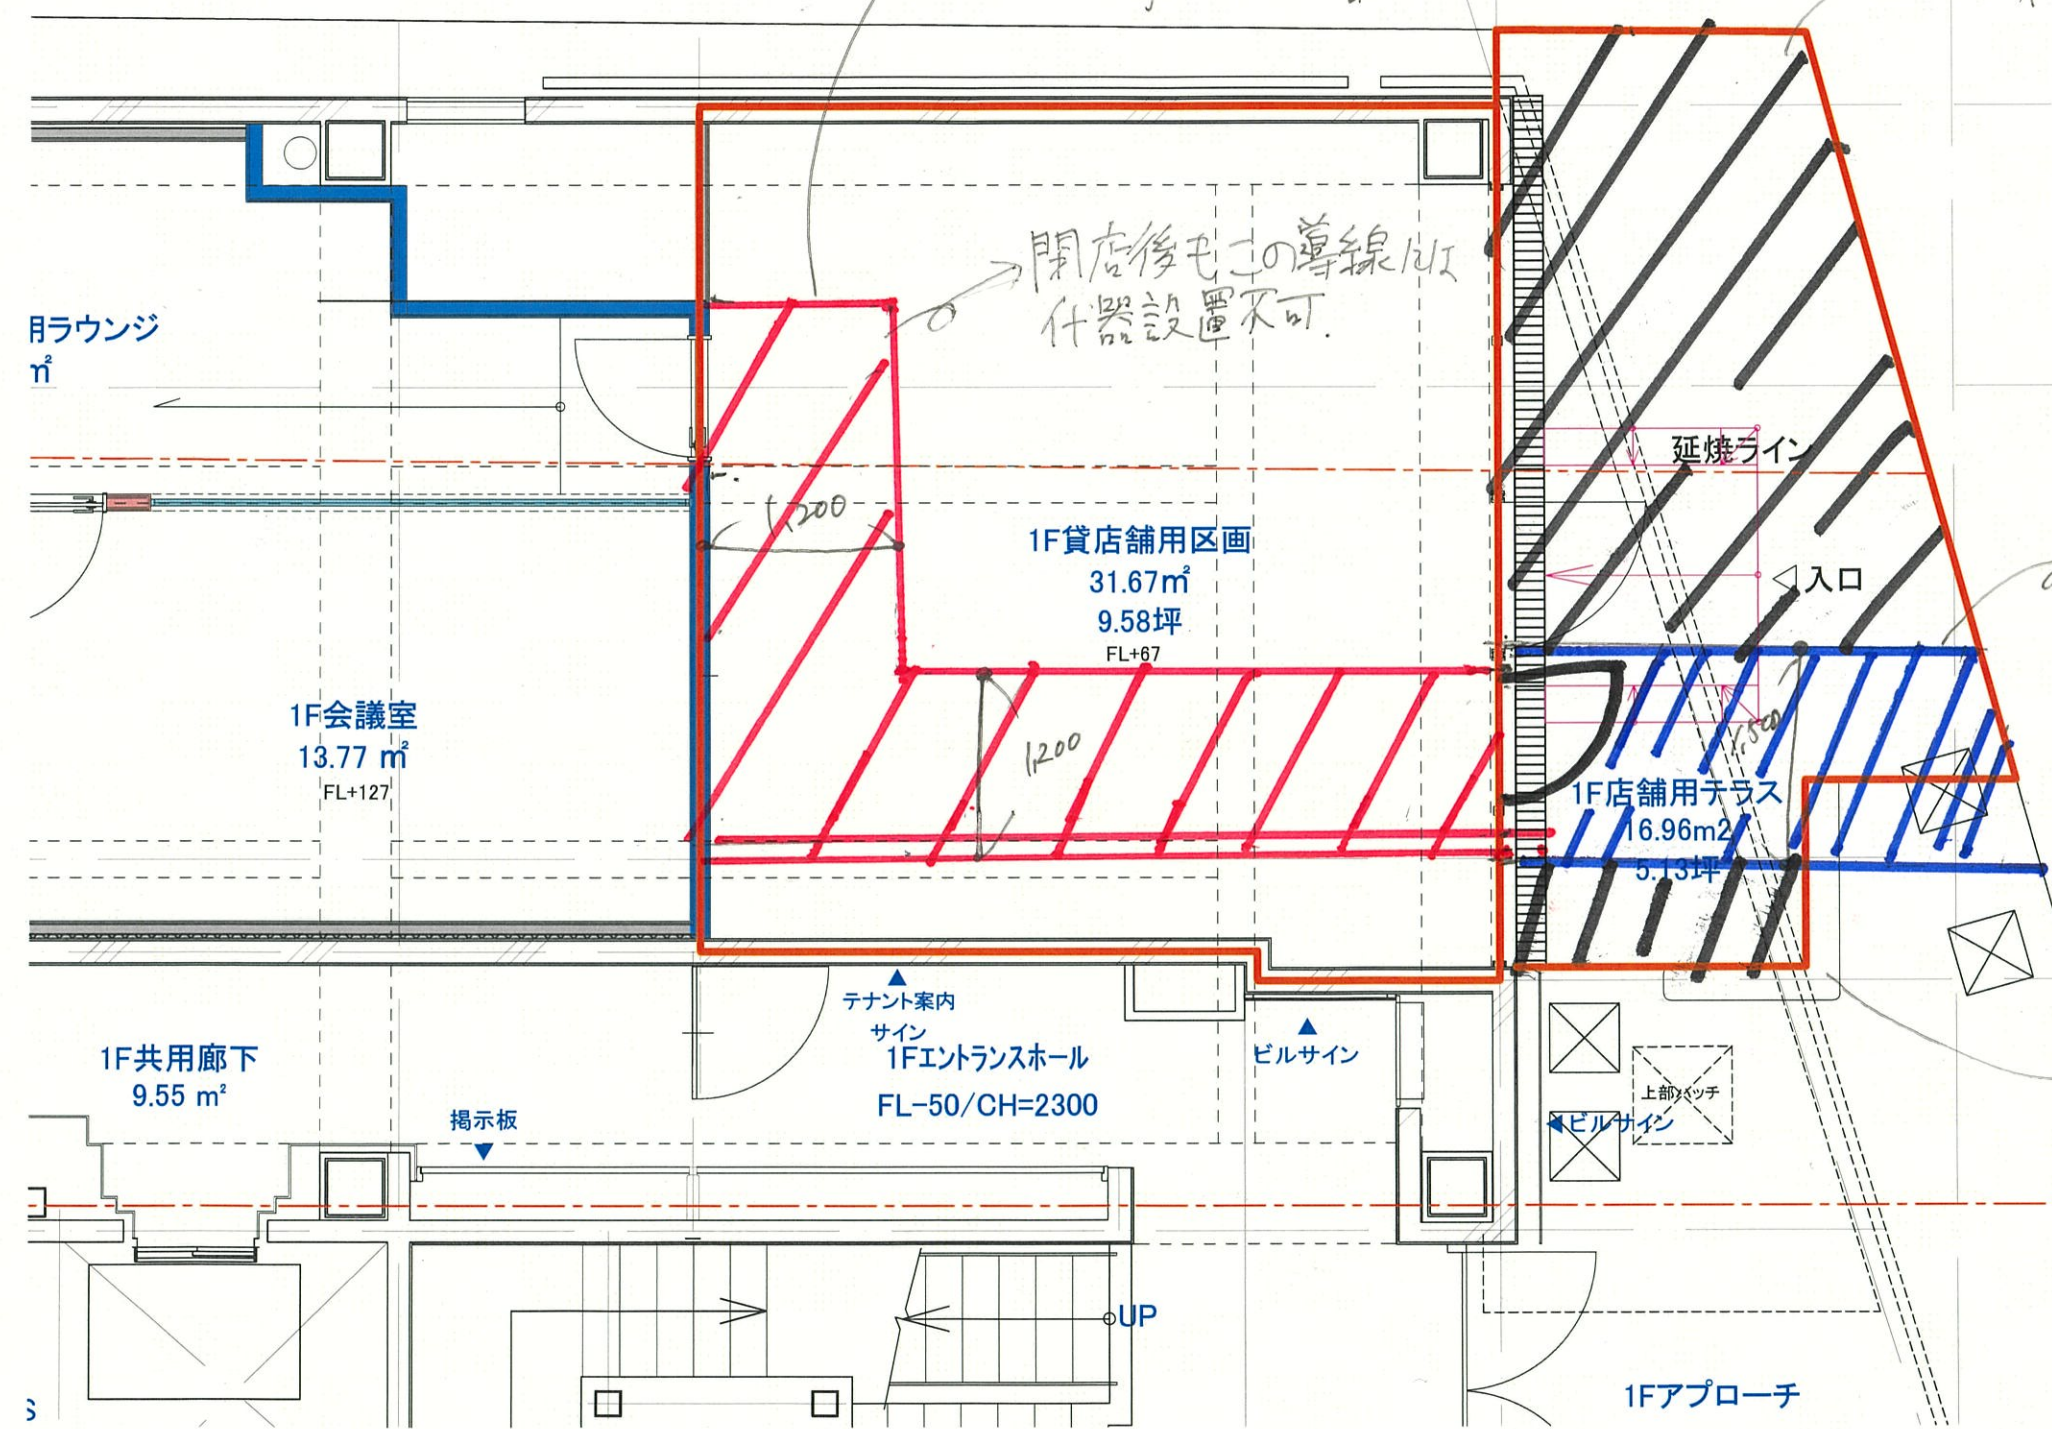

訂正年月日	訂正内容	訂正年月日	訂正内容	特記事項	工事番号	予定工期	作成日	建物名称	図面No.
							2026.05.14	BIGI青葉台	04
					承認印	検図	修正日	青葉台3丁目ビルリニューアルプロジェクト	縮尺
						営業		図面名称	A3:S=1/50
						製図		図面詳細名	

〒151-0053 東京都渋谷区渋谷3-8-12
渋谷第一生命ビルディング5階
一級建築士事務所 東京都知事登録 第64528号

三井ビル