

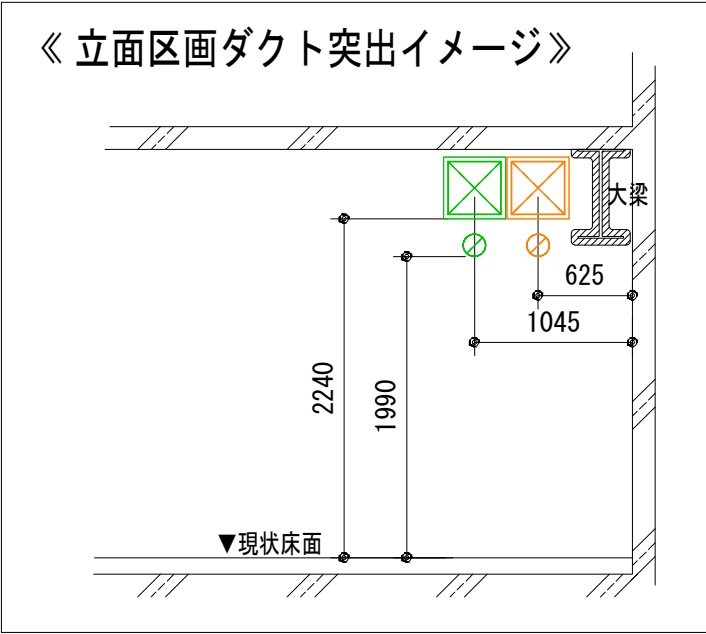


※計画段階の為現場調整にて位置の変更があるものとする。

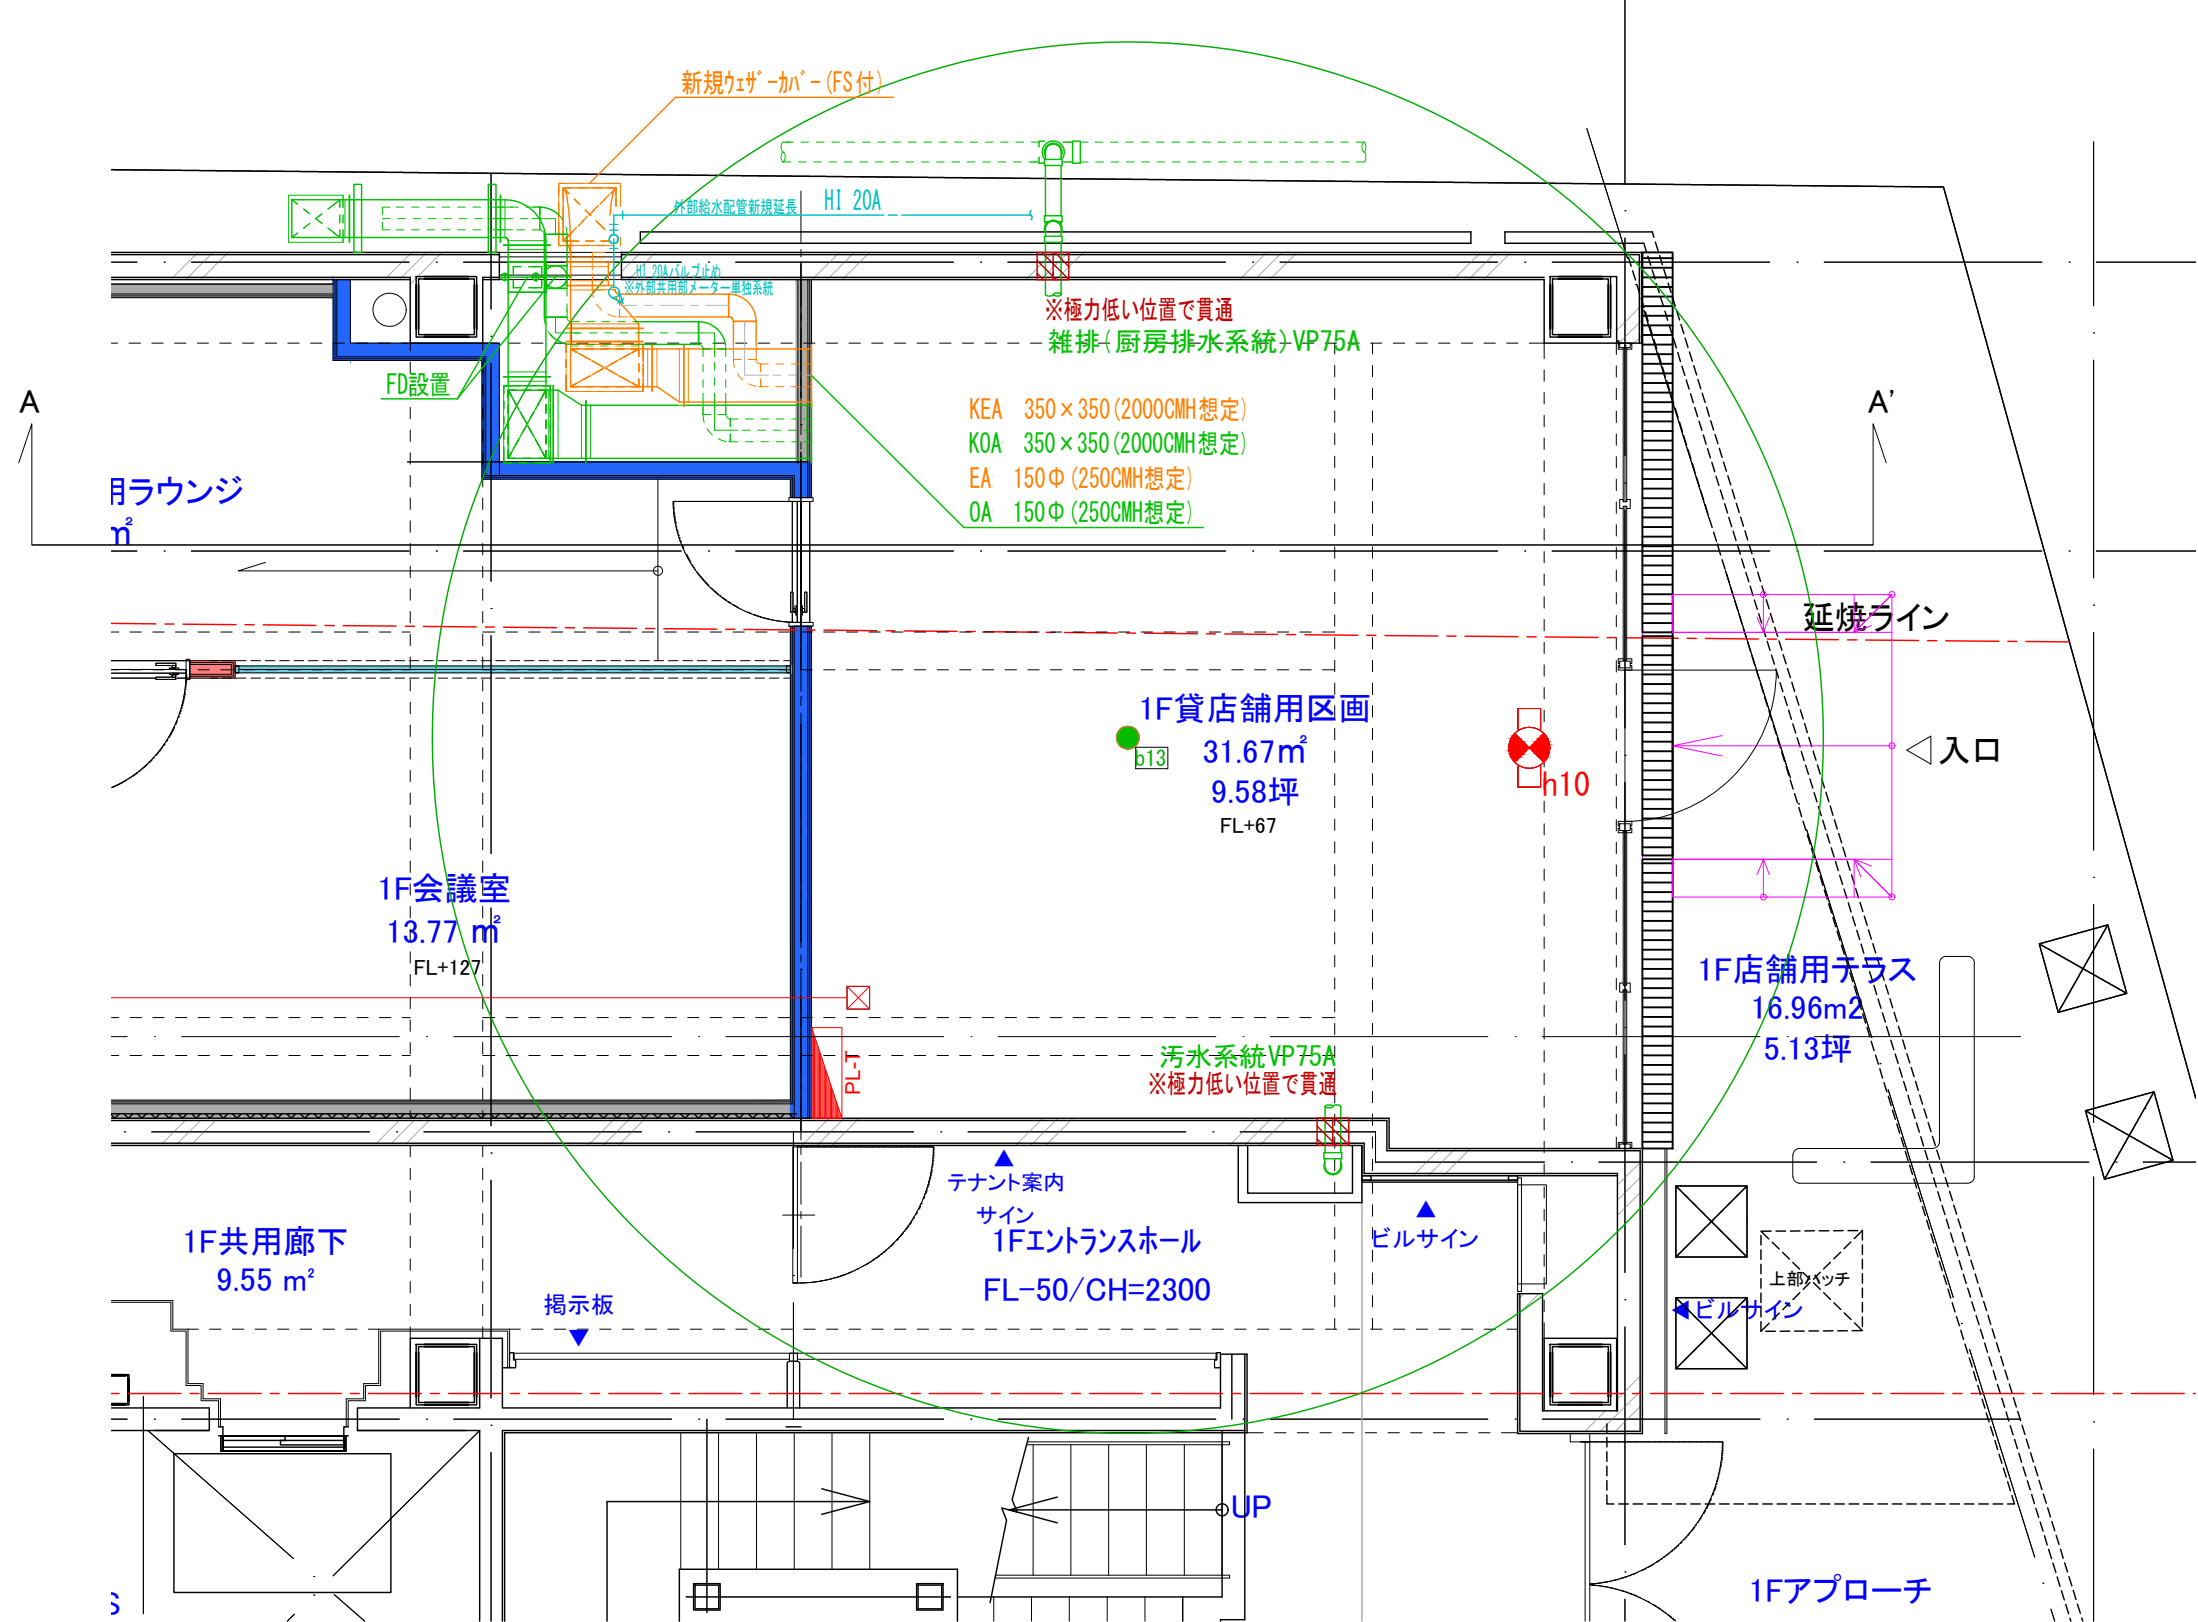

■ 凡例


- 直付非常照明13形
- 直付片面避難口誘導灯(C級)
- 弱電配管
- 店舗用分電盤

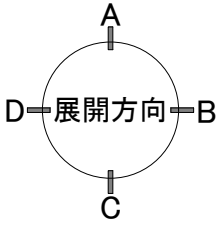

訂正年月日	訂正内容	訂正年月日	訂正内容	特記事項	イリス 〒151-0053 東京都渋谷区渋谷3-8-12 渋谷第一生命ビルディング5階 一級建築士事務所 東京都知事登録 第64528号	工事番号	予定工期	作成日	2026.05.14	建物名称	BIGI青葉台	図面No.	01
						承認印	検図	営業	製図	工事名称	青葉台3丁目ビルリニューアルプロジェクト	縮尺	A3: S=1/50
										図面名称	平面図		
										図面詳細名			

※計画段階の為現場調整にて位置の変更があるものとする。


1F貸店舗用区画

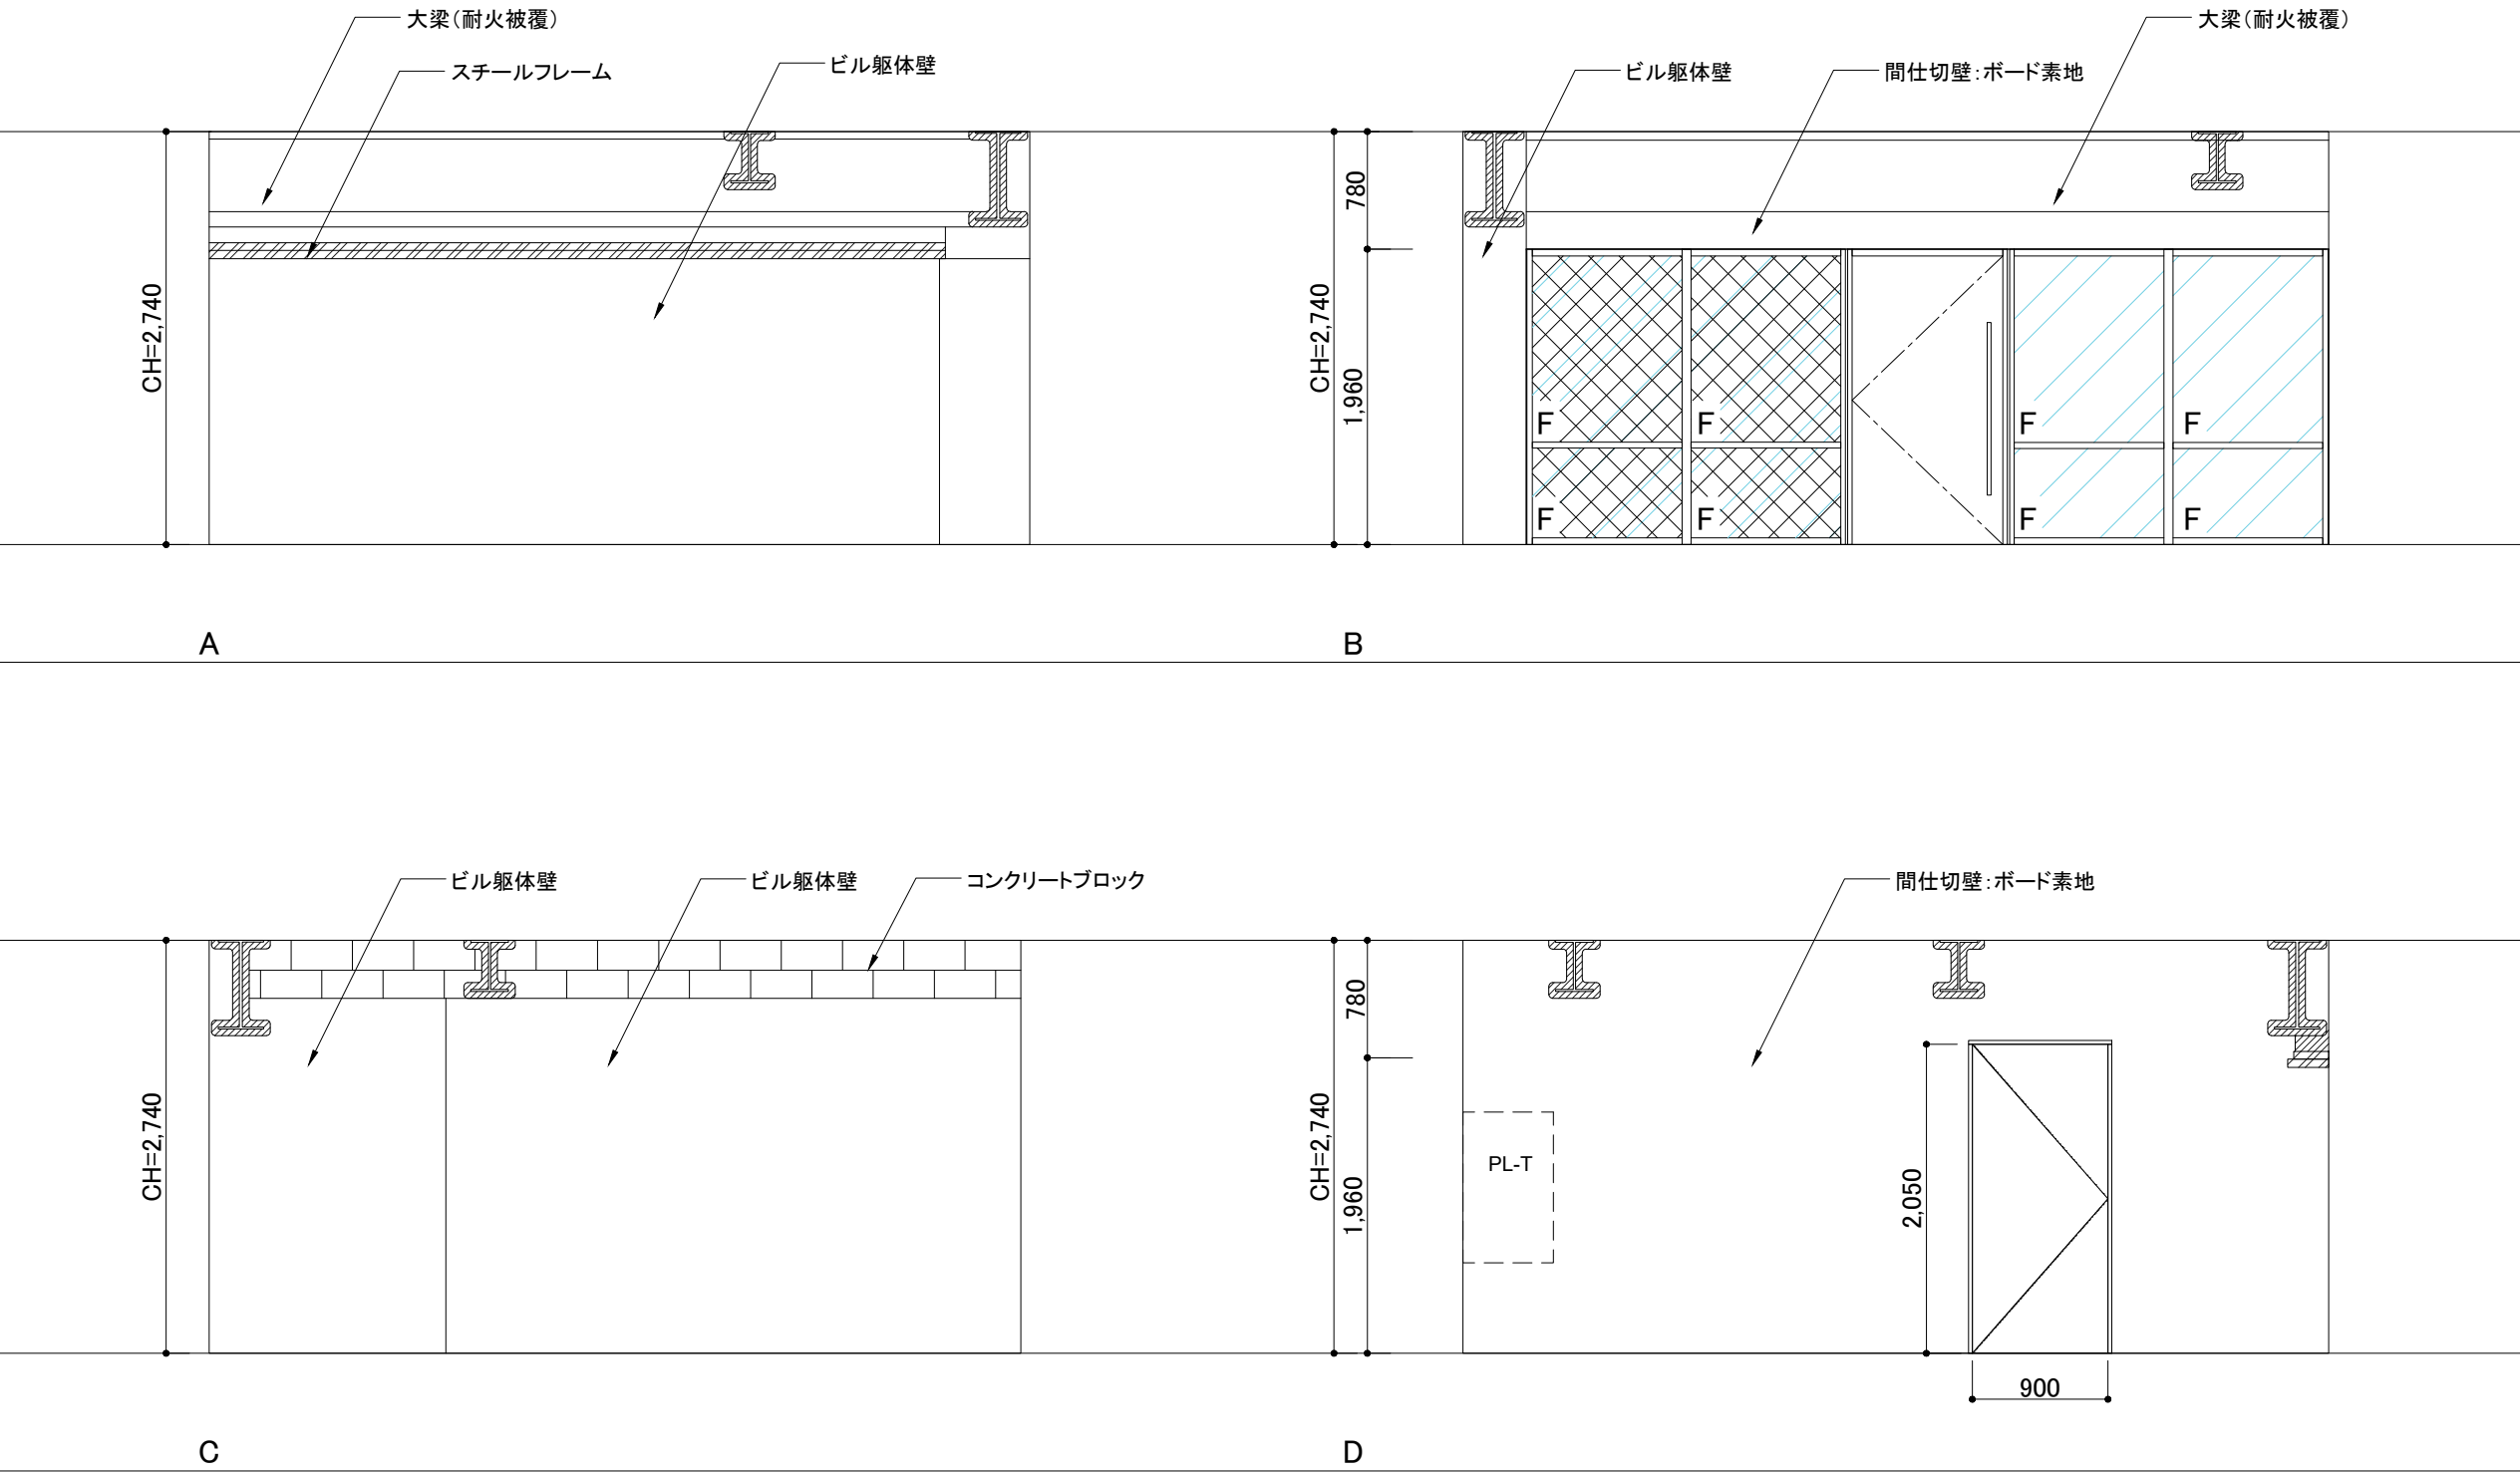


訂正履歴	訂正年月日	訂正内容	訂正年月日	訂正内容	特記事項	アールエス 〒151-0053 東京都渋谷区渋谷3-8-12 渋谷第一生命ビルディング5階 一級建築士事務所 東京都知事登録 第64528号	工事番号			予定工期			作成日 2026.05.14			建物名称 BIGI青葉台		図面No. 02
							承認印			検図 営業 製図			修正日			工事名称 青葉台3丁目ビルリニューアルプロジェクト		
																図面名称 展開図		縮尺 A3:S=1/50
																図面詳細名		

※計画段階の為現場調整にて位置の変更があるものとする。

1F貸店舗用区画

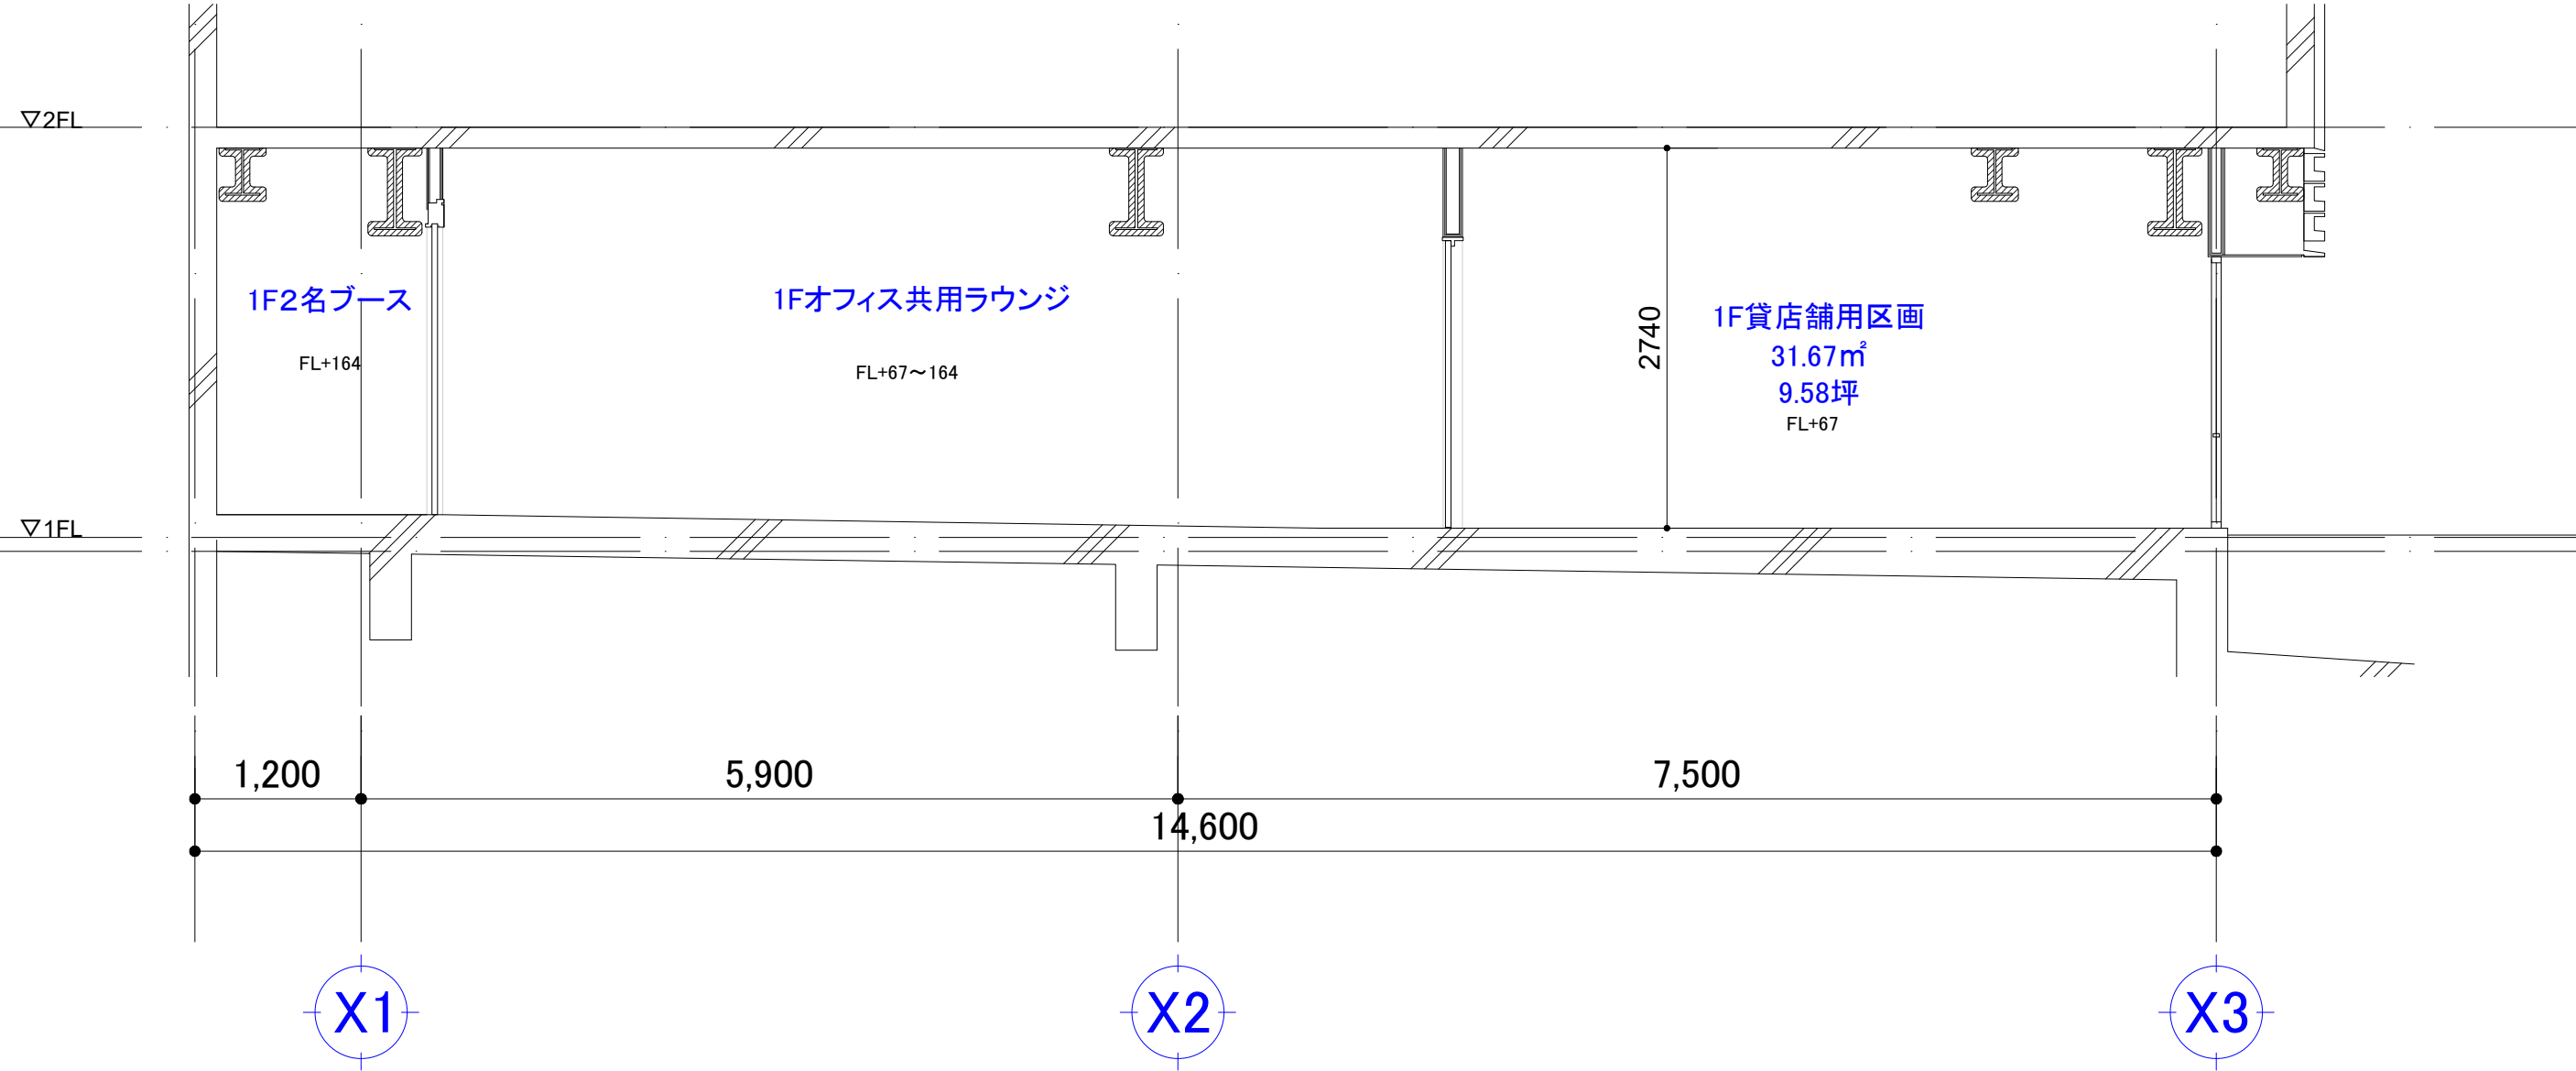

訂正履歴	訂正年月日	訂正内容	訂正年月日	訂正内容	特記事項	エイト 〒151-0053 東京都渋谷区渋谷3-8-12 渋谷第一生命ビルディング5階 一級建築士事務所 東京都知事登録 第64528号	工事番号			予定工期			作成日	2026.05.14	建物名称	BIGI青葉台	図面No.	03
							承認印			検図			修正日		工事名称	青葉台3丁目ビルリニューアルプロジェクト	縮尺	A3:S=1/50
										営業					図面名称	A-A'断面図		
										製図					図面詳細名			

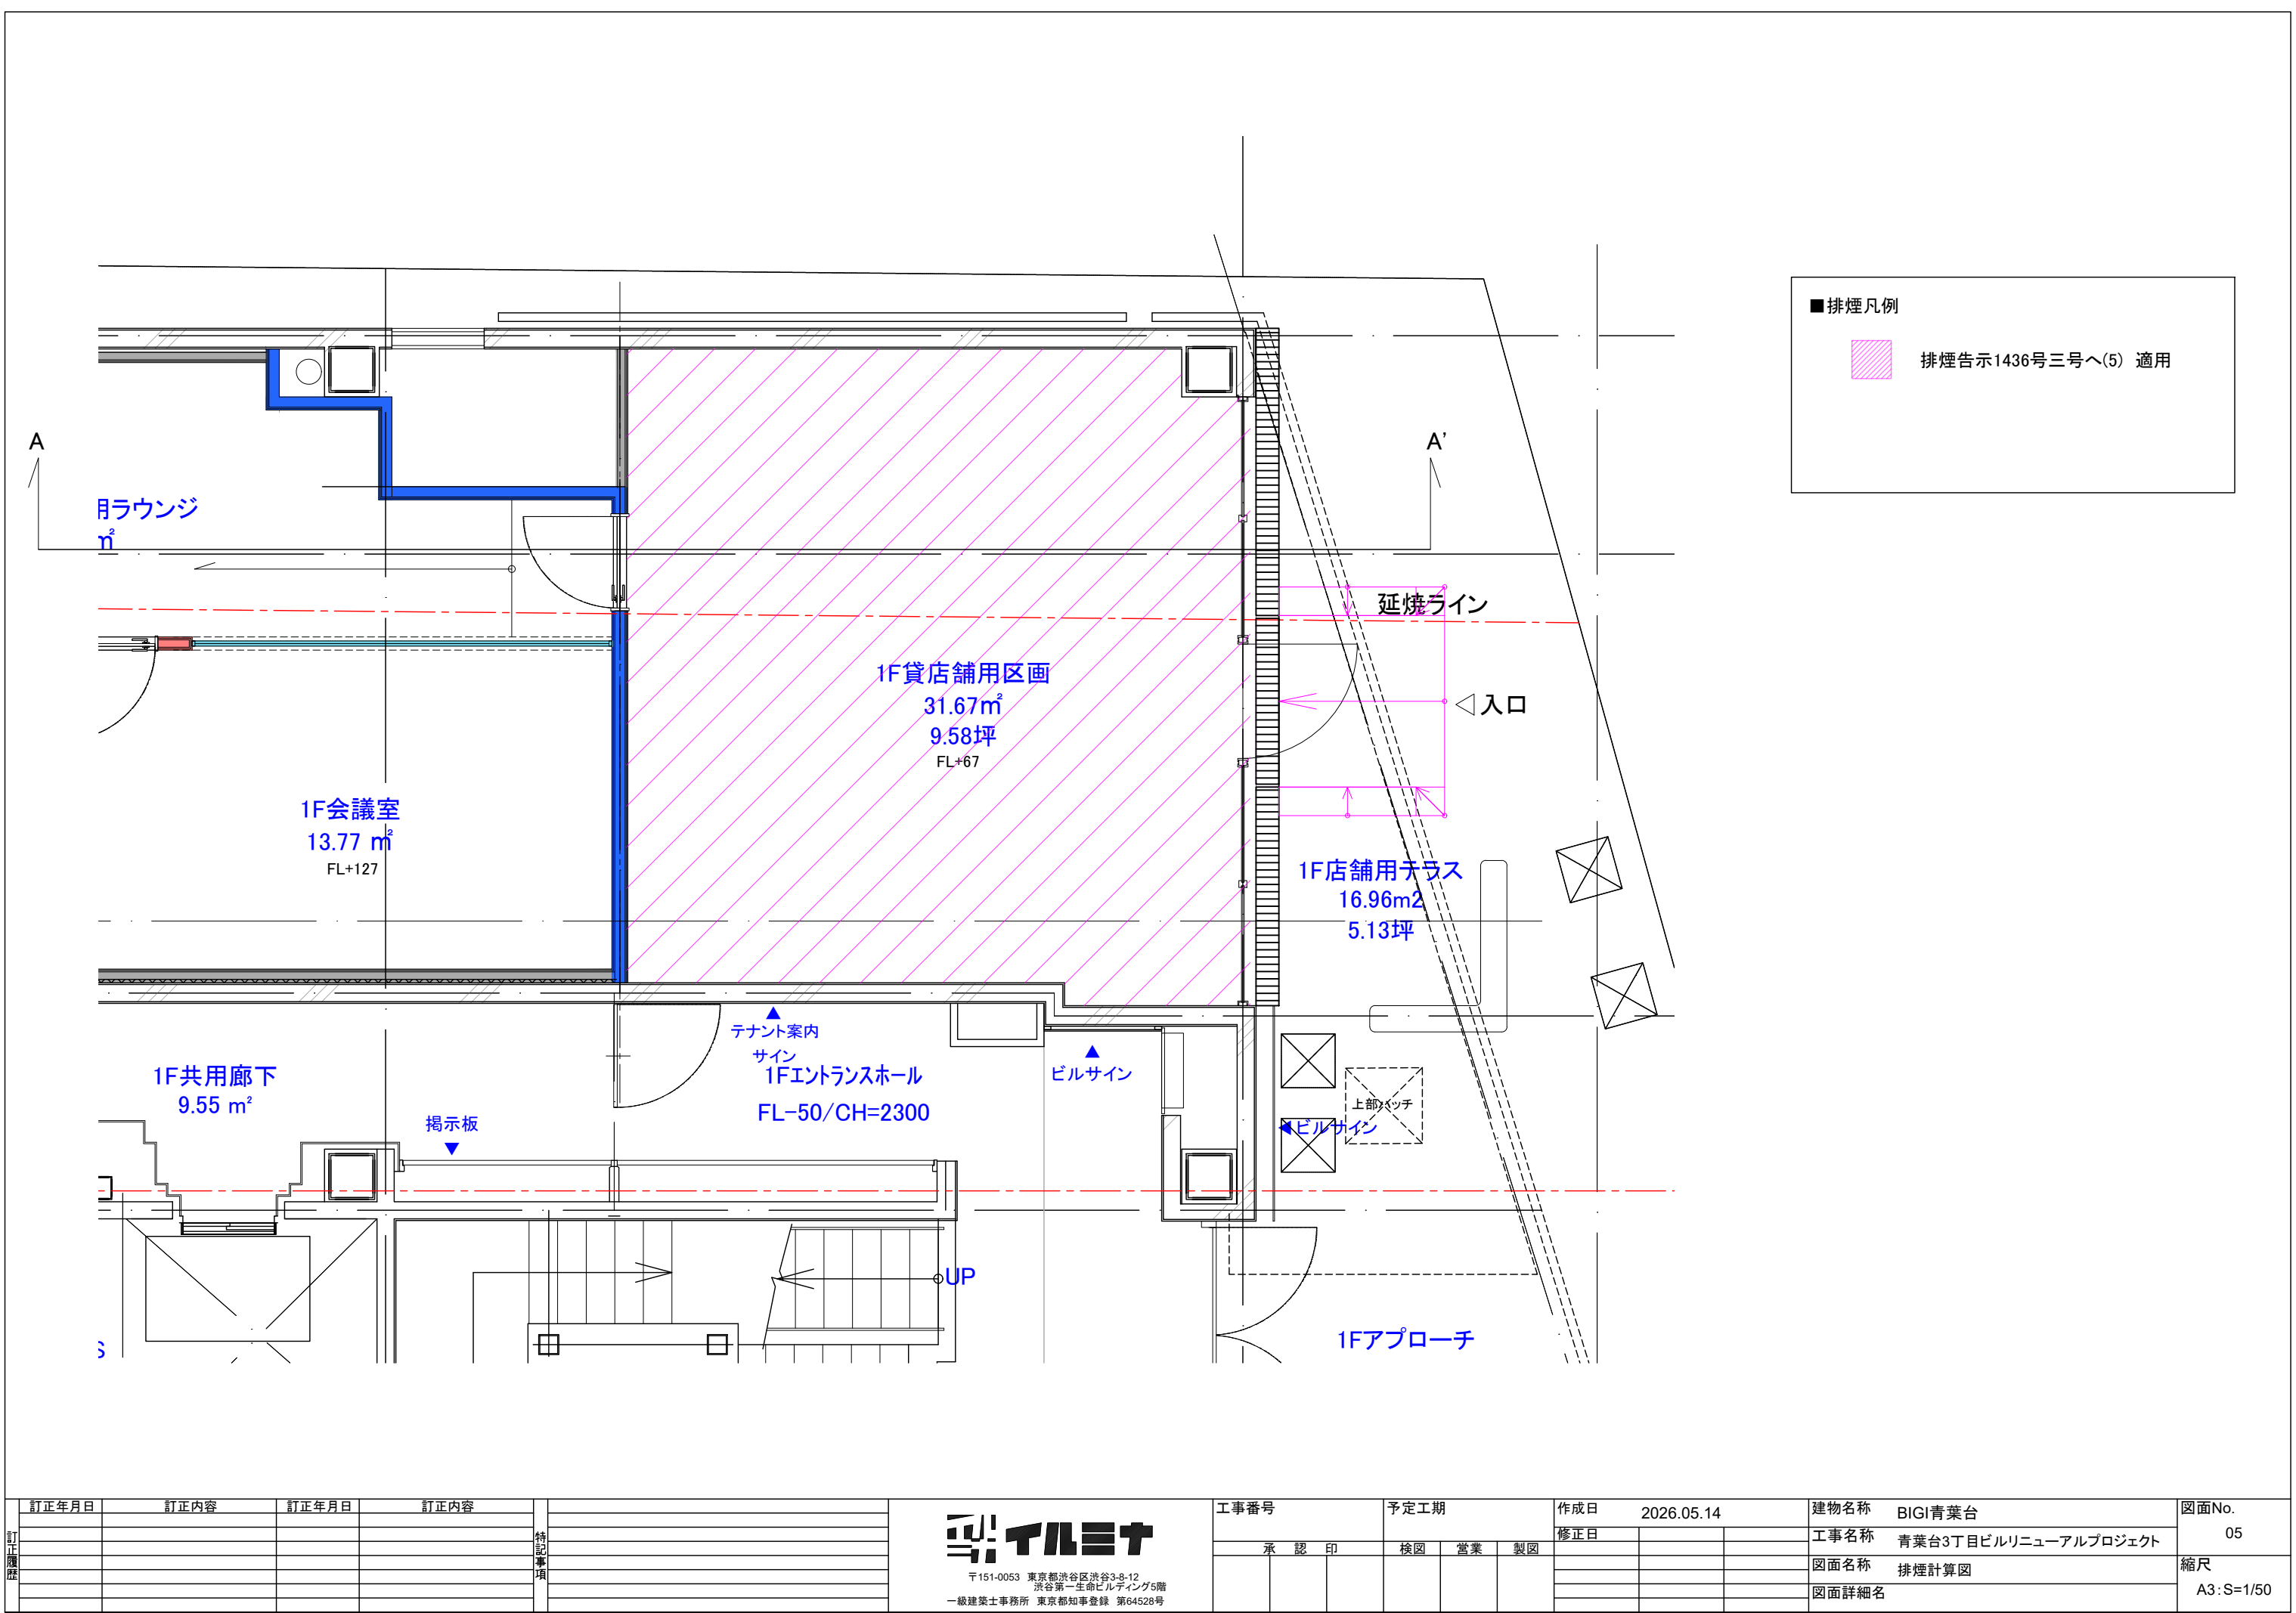

訂正履歴	訂正年月日	訂正内容	訂正年月日	訂正内容	特記事項	 〒151-0053 東京都渋谷区渋谷3-8-12 渋谷第一生命ビルディング5階 一級建築士事務所 東京都知事登録 第64528号	工事番号			予定工期			作成日 2026.05.14			建物名称 BIGI青葉台		図面No. 05
							承認印			検図 営業 製図			修正日			工事名称 青葉台3丁目ビルリニューアルプロジェクト		
																図面名称 排煙計算図		縮尺 A3:S=1/50
																図面詳細名		